


1.5MLD MBR BASED STP TENTATIVE PLAN, K.V.G. MEDICAL COLLEGE & HOSPITAL, SULLIA

KEY PLAN:

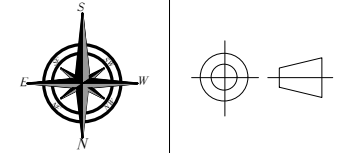

GENERAL NOTES:

- THIS DRAWING IS THE PROPERTY OF AAPAAVANI. DUPLICATION OF THESE DRAWINGS IN ANY MODEL IS PROHIBITED.
- DO NOT SCALE THE DRAWINGS, READ THE WRITTEN DIMENSIONS.
- ANY DISCREPANCY HAS TO BE REPORTED TO THE CONSULTANTS.
- PLAN MAY CHANGE AS PER SITE CONDITIONS.

FOR APPROVAL	REV	DATE	REMARK
	(R1)		
	(R2)		
	(R3)		
	(R4)		

LEGEND	
---	GUIDE LINE
---	CORE CUTTING

DATE: 30/07/2026 SCALE: NTS

DWG NO: AES/KVG/STP/PLN-01

ALL DIMENSIONS ARE IN METER

PROJECT TITLE:

GENERAL ARRANGEMENT DRAWING

DRAWN BY: PRP

DESIGNED BY: PRP


CONSULTANTS:

 AAPAAVANI ENVIRONMENTAL SOLUTIONS PVT LTD
SHED NO C-51, INDUSTRIAL AREA
BEHIND BANK OF BARODA,
BAIKAMPADY, MANGALORE DK-575011
Phone: 9980584372, 8147901288
E-mail: projects@aapaavani.com


CLIENT:

K.V.G. MEDICAL COLLEGE & HOSPITAL,
SULLIA


PLAN

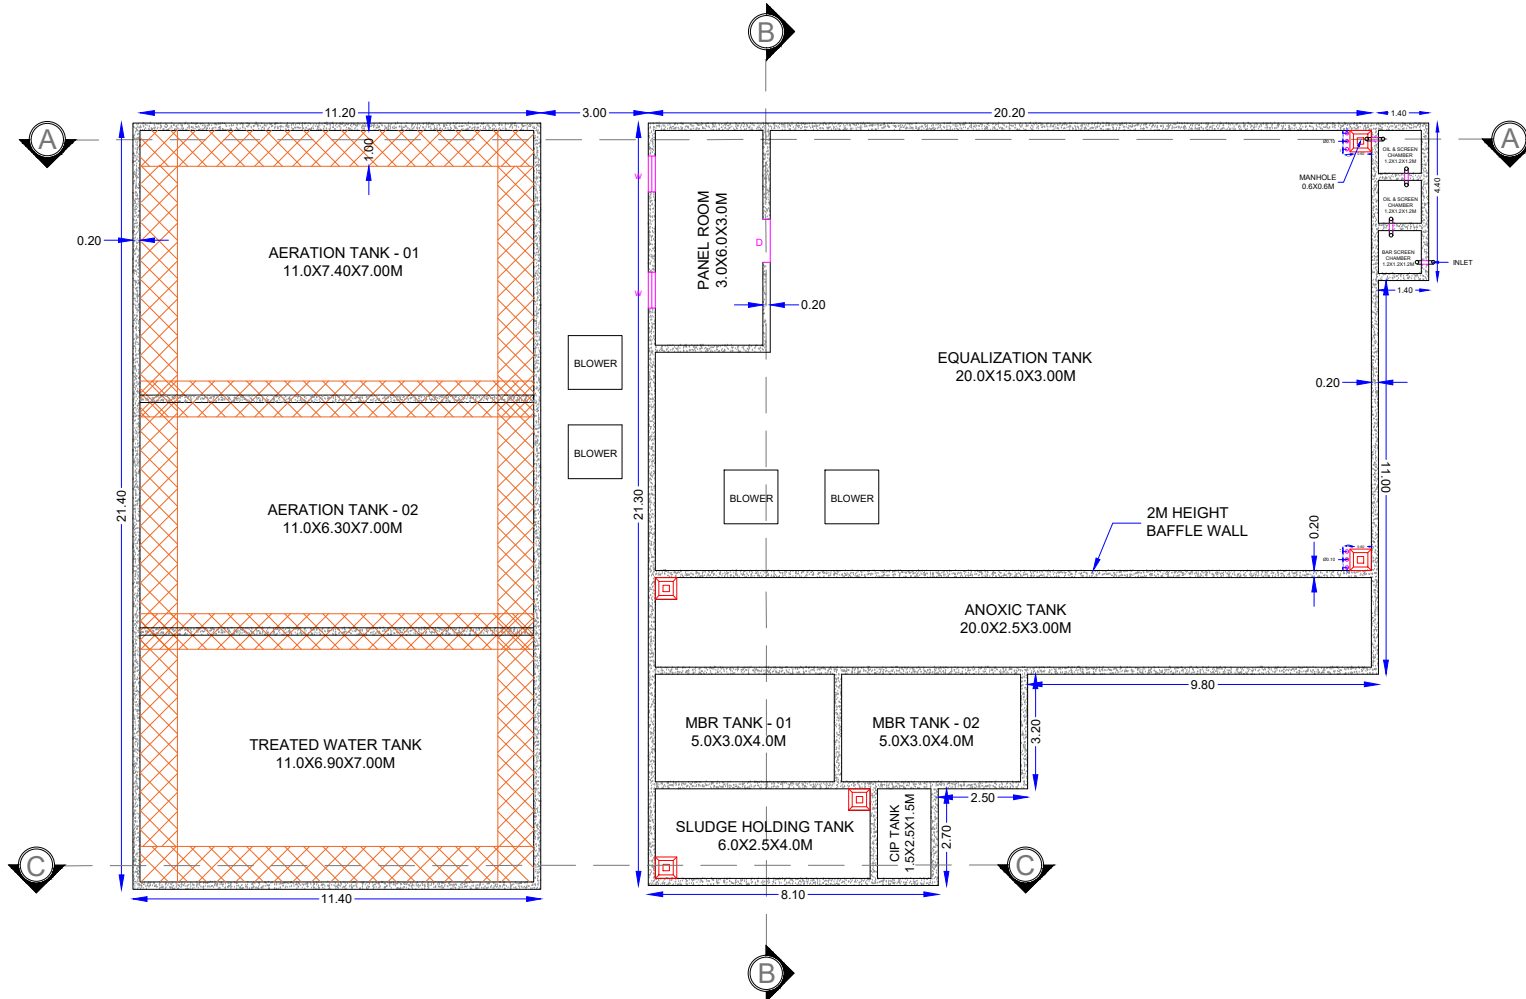


1.5MLD MBR BASED STP TENTATIVE PLAN, K.V.G. MEDICAL COLLEGE & HOSPITAL, SULLIA

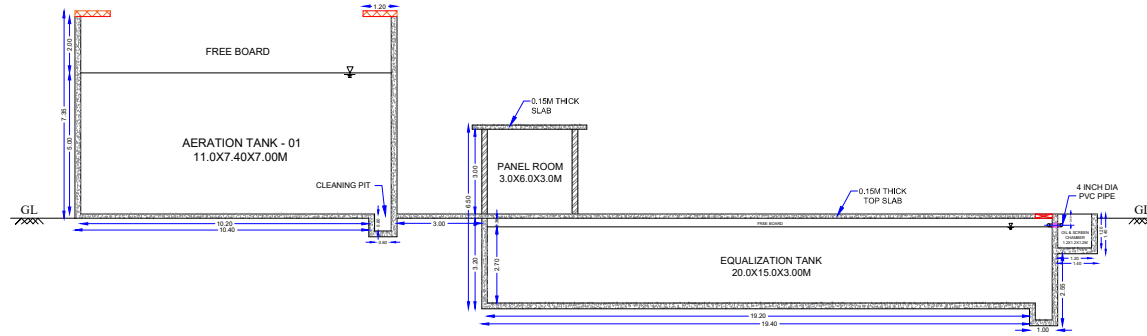

CROSS SECTION ALONG A-A

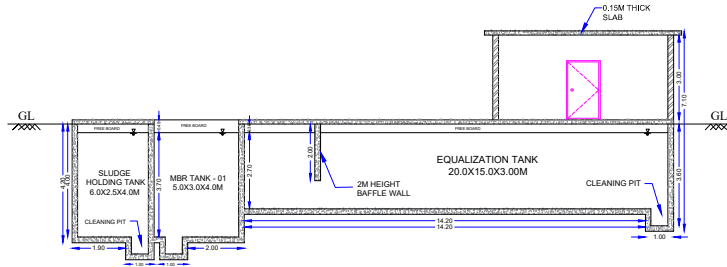


CROSS SECTION ALONG B-B

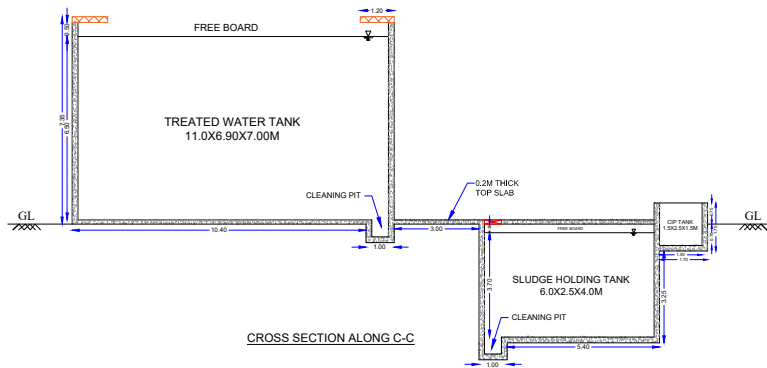

CROSS SECTION ALONG C-C

KEY PLAN:

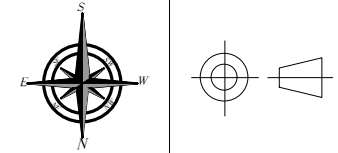

GENERAL NOTES:

- THIS DRAWING IS THE PROPERTY OF AAPAAVANI. DUPLICATION OF THESE DRAWINGS IN ANY MODEL IS PROHIBITED.
- DO NOT SCALE THE DRAWINGS, READ THE WRITTEN DIMENSIONS.
- ANY DISCREPANCY HAS TO BE REPORTED TO THE CONSULTANTS.
- PLAN MAY CHANGE AS PER SITE CONDITIONS.

FOR APPROVAL

REV	DATE	REMARK
(R1)		
(R2)		
(R3)		
(R4)		

LEGEND

---	GUIDE LINE
---	CORE CUTTING

DATE: 30/07/2026 SCALE: NTS

DWG NO: AES/KVG/STP/PLN-01

ALL DIMENSIONS ARE IN METER

PROJECT TITLE:

GENERAL ARRANGEMENT DRAWING

DRAWN BY: PRP

DESIGNED BY: PRP

CONSULTANTS:



AAPAAVANI ENVIRONMENTAL
SOLUTIONS PVT LTD
SHED NO C-51, INDUSTRIAL AREA
BEHIND BANK OF BARODA,
BAIKAMPADY, MANGALORE DK-575011
Phone: 9980584372, 8147901288
E-mail: projects@aapaavani.com

CLIENT:

K.V.G. MEDICAL COLLEGE & HOSPITAL,
SULLIA

The contents of this document/drawing were developed using intellectual property owned by Aapaavani Environmental Solutions Pvt. Ltd. It contains confidential and proprietary information that remains the sole property of the company. This material is intended exclusively for use in connection with activities authorized by Aapaavani Environmental Solutions Pvt. Ltd. © All rights to this drawing are reserved by the company.