

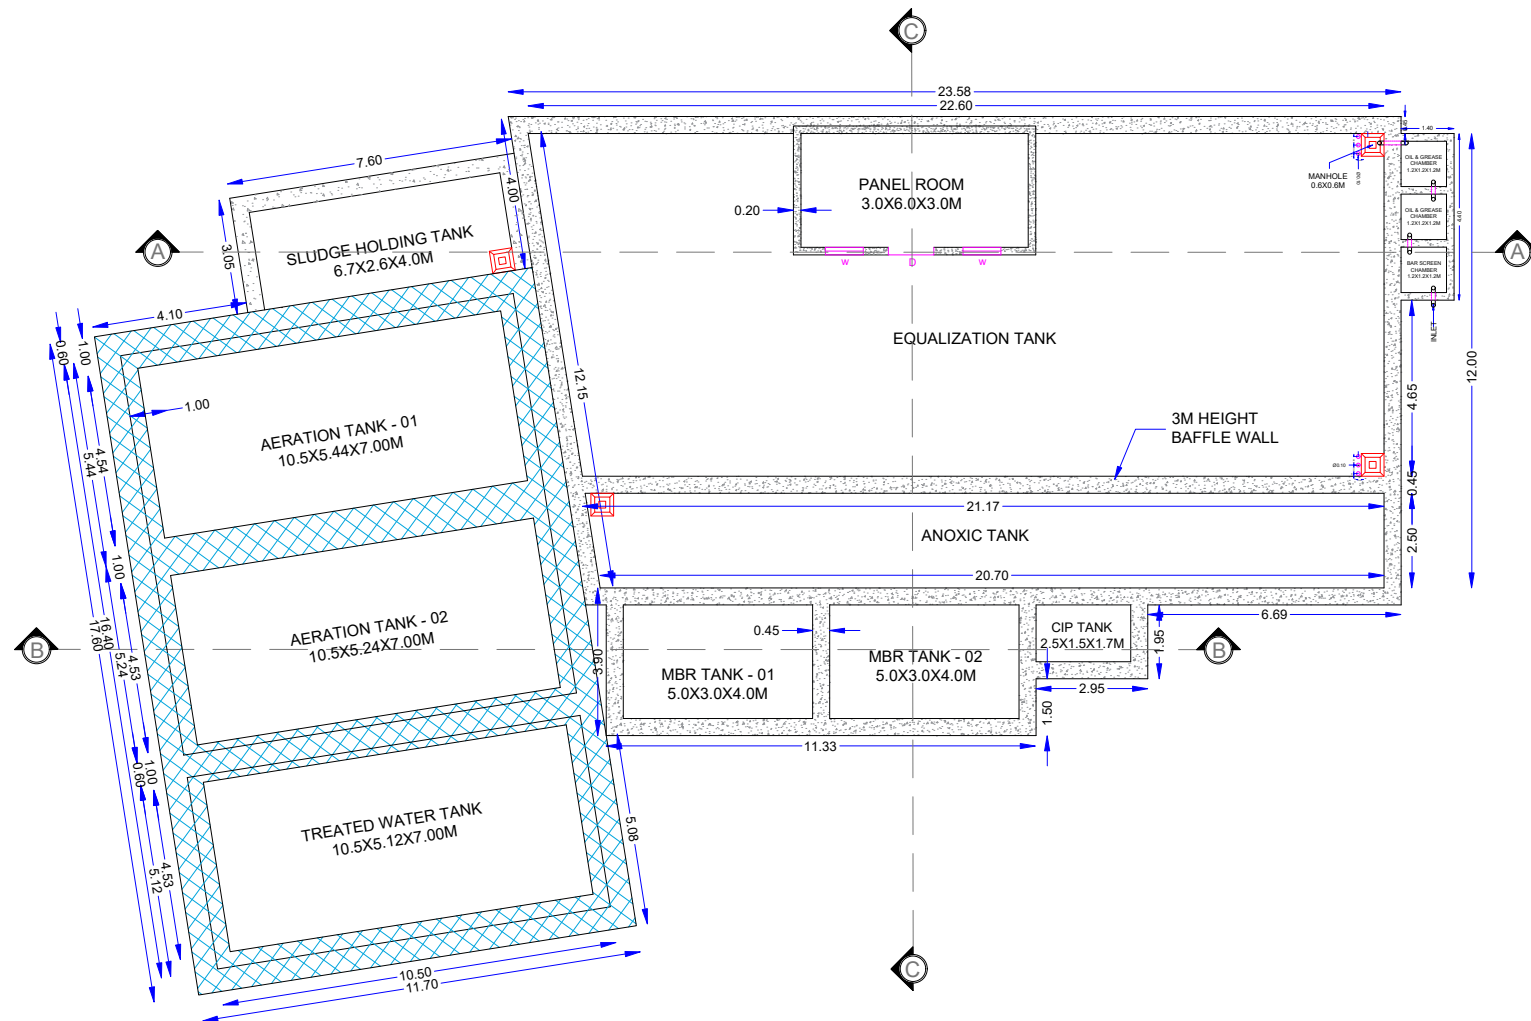


1.5MLD MBR BASED STP TENTATIVE PLAN, K.V.G. MEDICAL COLLEGE & HOSPITAL, SULLIA

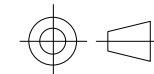

PLAN

KEY PLAN:

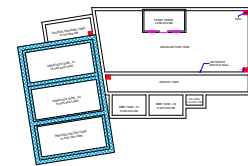

GENERAL NOTES:

- THIS DRAWING IS THE PROPERTY OF AAPAAVANI. DUPLICATION OF THESE DRAWINGS IN ANY MODEL IS PROHIBITED.
- DO NOT SCALE THE DRAWINGS, READ THE WRITTEN DIMENSIONS.
- ANY DISCREPANCY HAS TO BE REPORTED TO THE CONSULTANTS.
- PLAN MAY CHANGE AS PER SITE CONDITIONS.

FOR APPROVAL	REV	DATE	REMARK
	(R1)		
	(R2)		
	(R3)		
	(R4)		

LEGEND

---	GUIDE LINE
---	CORE CUTTING

DATE: 25/08/2026 SCALE: NTS

DWG NO: AES/KVG/STP/PLN-01

ALL DIMENSIONS ARE IN METER

PROJECT TITLE:

GENERAL ARRANGEMENT DRAWING

DRAWN BY: PRP

DESIGNED BY: PRP

CONSULTANTS:

AAPAAVANI ENVIRONMENTAL SOLUTIONS PVT LTD
 SHED NO C-51, INDUSTRIAL AREA
 BEHIND BANK OF BARODA,
 BAIKAMPADY, MANGALORE DK-575011
 Phone: 9980584372, 8147901288
 E-mail: projects@aapaavani.com

CLIENT:

K.V.G. MEDICAL COLLEGE & HOSPITAL,
 SULLIA