




200KLD STP PLAN, K.V.G. AYURVEDA MEDICAL COLLEGE, SULLIA

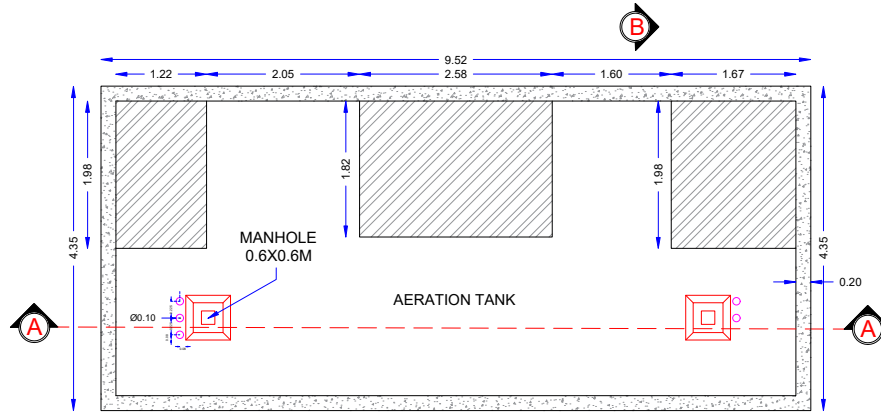

PLAN


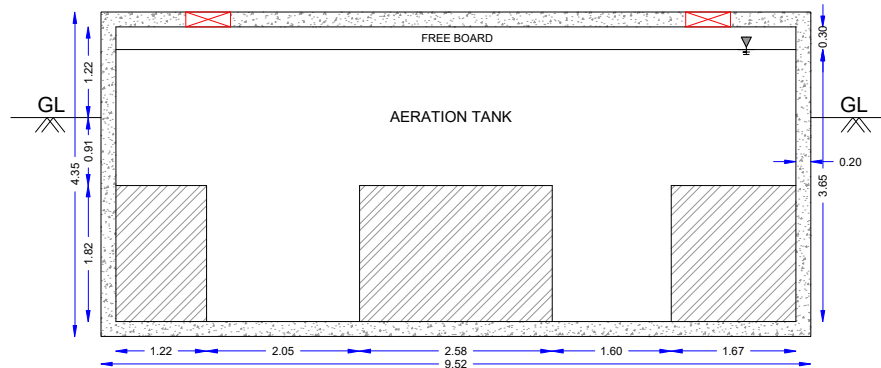


CROSS SECTION ALONG A - A

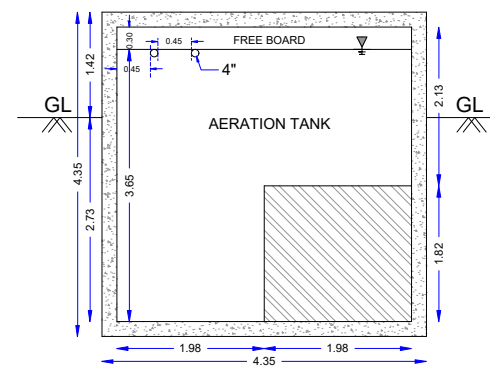

CROSS SECTION ALONG B - B

KEY PLAN:

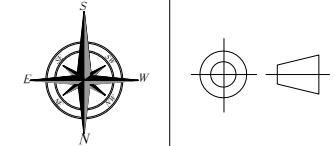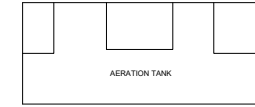

GENERAL NOTES:

- THIS DRAWING IS THE PROPERTY OF AAPAAVANI. DUPLICATION OF THESE DRAWINGS IN ANY MODEL IS PROHIBITED.
- DO NOT SCALE THE DRAWINGS, READ THE WRITTEN DIMENSIONS.
- ANY DISCREPANCY HAS TO BE REPORTED TO THE CONSULTANTS.
- PLAN MAY CHANGE AS PER SITE CONDITIONS.

FOR APPROVAL

REV	DATE	REMARK
(R1)		
(R2)		
(R3)		
(R4)		

LEGEND

	EXISTING FOOTING
--	------------------

DATE: 28/09/2026

SCALE: NTS

DWG NO: AES/KVG/STP/PLN/SEC-01

ALL DIMENSIONS ARE IN METER

PROJECT TITLE:

GENERAL ARRANGEMENT DRAWING

DRAWN BY:

PRP

DESIGNED BY:

PRP

CONSULTANTS:



AAPAAVANI ENVIRONMENTAL SOLUTIONS PVT LTD
SHED NO C-54, INDUSTRIAL AREA
BEHIND BANK OF BARODA,
BAIKAMPADY, MANGALORE DK-575011
Phone: 9980584372, 8147901288
E-mail: projects@apaavani.com

CLIENT:

K.V.G. AYURVEDA MEDICAL COLLEGE,
SULLIA