

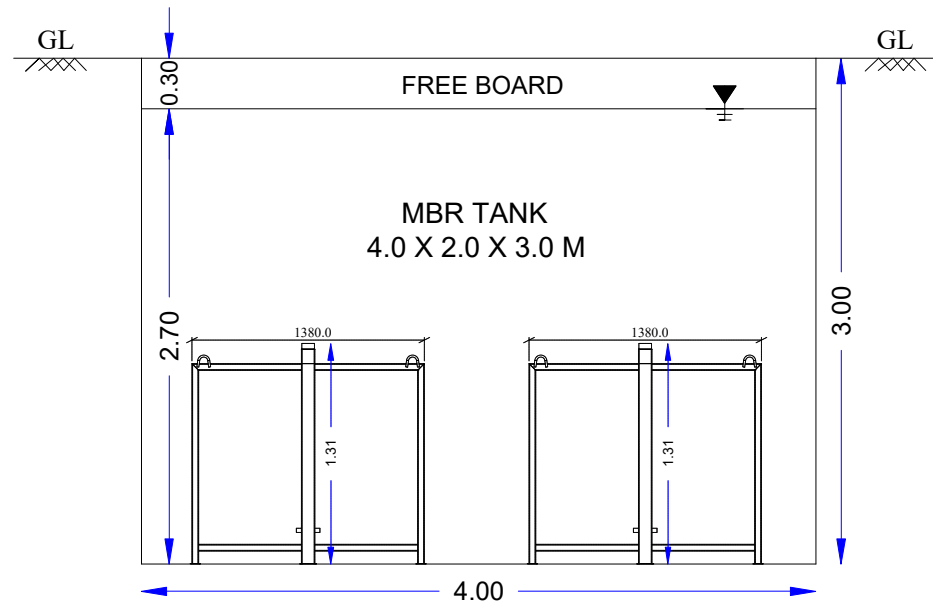


# 200KLD STP MBR TANK PLAN, K.V.G. AYURVEDA MEDICAL COLLEGE, SULLIA

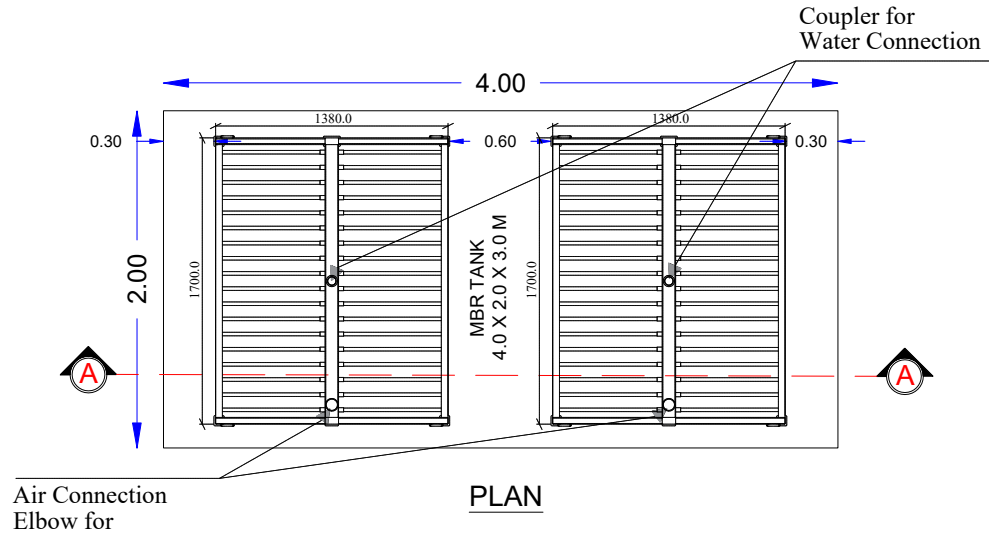

## KEY PLAN:

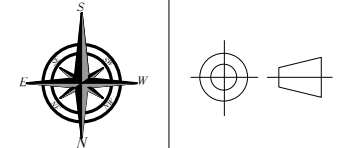

## GENERAL NOTES:

- THIS DRAWING IS THE PROPERTY OF AAPAAVANI. DUPLICATION OF THESE DRAWINGS IN ANY MODEL IS PROHIBITED.
- DO NOT SCALE THE DRAWINGS, READ THE WRITTEN DIMENSIONS.
- ANY DISCREPANCY HAS TO BE REPORTED TO THE CONSULTANTS.
- PLAN MAY CHANGE AS PER SITE CONDITIONS.

FOR APPROVAL

| REV  | DATE | REMARK |
|------|------|--------|
| (R1) |      |        |
| (R2) |      |        |
| (R3) |      |        |
| (R4) |      |        |
| (R5) |      |        |

DATE: 29/09/2026

SCALE: NTS

DWG NO: AES/KVG/STP/PLN/SEC-01

ALL DIMENSIONS ARE IN METER

PROJECT TITLE:

GENERAL ARRANGEMENT DRAWING

DRAWN BY:

PRP

DESIGNED BY:

PRP

## CONSULTANTS:



AAPAAVANI ENVIRONMENTAL SOLUTIONS PVT LTD  
SHED NO C-54, INDUSTRIAL AREA  
BEHIND BANK OF BARODA,  
BAIKAMPADY, MANGALORE DK-575011  
Phone: 9980584372, 8147901288  
E-mail: projects@aapaavani.com

## CLIENT:

K.V.G. AYURVEDA MEDICAL COLLEGE,  
SULLIA